

COMUNE DI GINOSA
Provincia di Taranto

GINOSA CICLABILE | PROGETTO PER LA REALIZZAZIONE
DI UN PERCORSO CICLABILE DI CONNESSIONE DEI
PRINCIPALI ATTRATTORI IN AMBITO URBANO

PR Puglia 2021-2027, Priorità III "Mobilità urbana sostenibile", Azione 3.1 "Interventi per la promozione della mobilità urbana multimodale sostenibile" - Sub Azione 3.1.2 - "Promuovere le infrastrutture ed i servizi di mobilità dolce ciclopedonale a scala urbana e suburbana."
Avviso per la selezione interventi finalizzati alla realizzazione di reti percorsi ciclabili e/o ciclopedonali in aree urbane e suburbane

PROGETTO ESECUTIVO

TAV. 8.3

STATO DI PROGETTO
(Via Poggio, Viale Martiri d'Ungheria)

SCALA
1:200


Committente
Comune di GINOSA

Il Responsabile Unico del Progetto:
Arch. Rosa Giacomello

Progettazione:
CITTA' FERTILE
ARCHITETTURA E INGEGNERIA

LIVELLO DI PROGETTAZIONE		NOME FILE	REV.	DATA	SOFT/STRUTTURA
U.E.	TAV. 8.3	06	Marzo 2024	7	


Il presente progetto (opera) è di esclusiva proprietà del progettista e cui relativi diritti dovranno essere attribuiti alle vigenti leggi. E' vietata la riproduzione o divulgazione senza autorizzazione scritta del progettista che si riserva di perseguire legalmente i trasgressori.

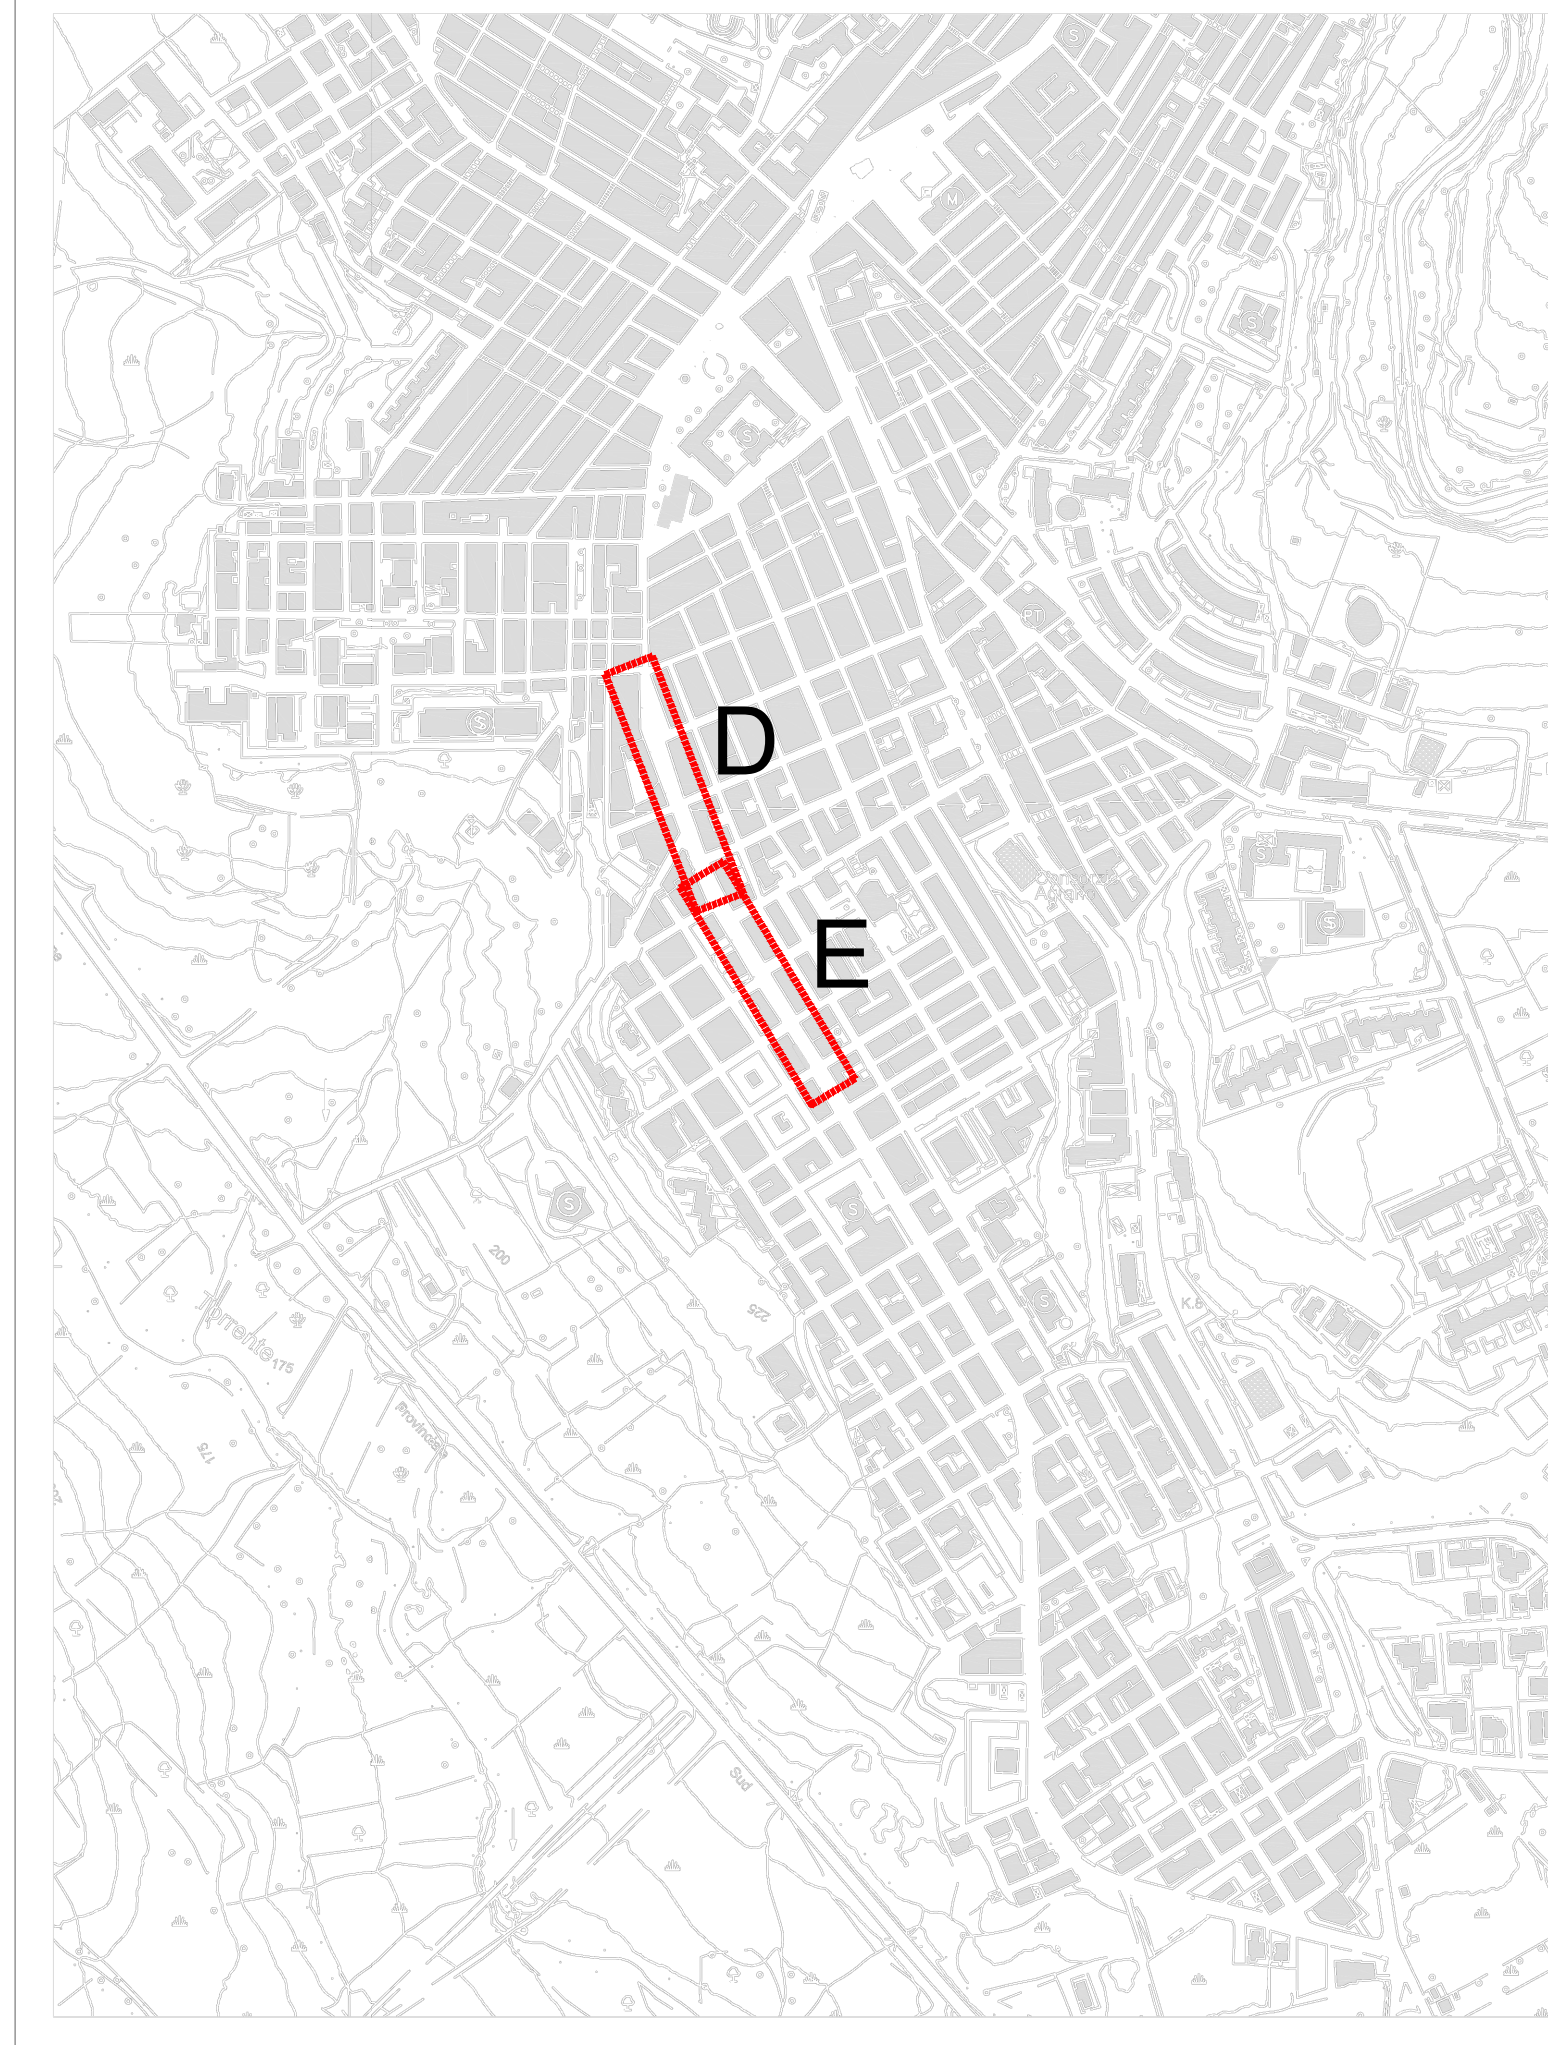


Planimetria generale di riferimento in Viale Martiri d'Ungheria




D_Viale Martiri d'Ungheria (Isolato 01 - 02 - 03 nel tratto compreso tra via Toti e via Bainsizza)

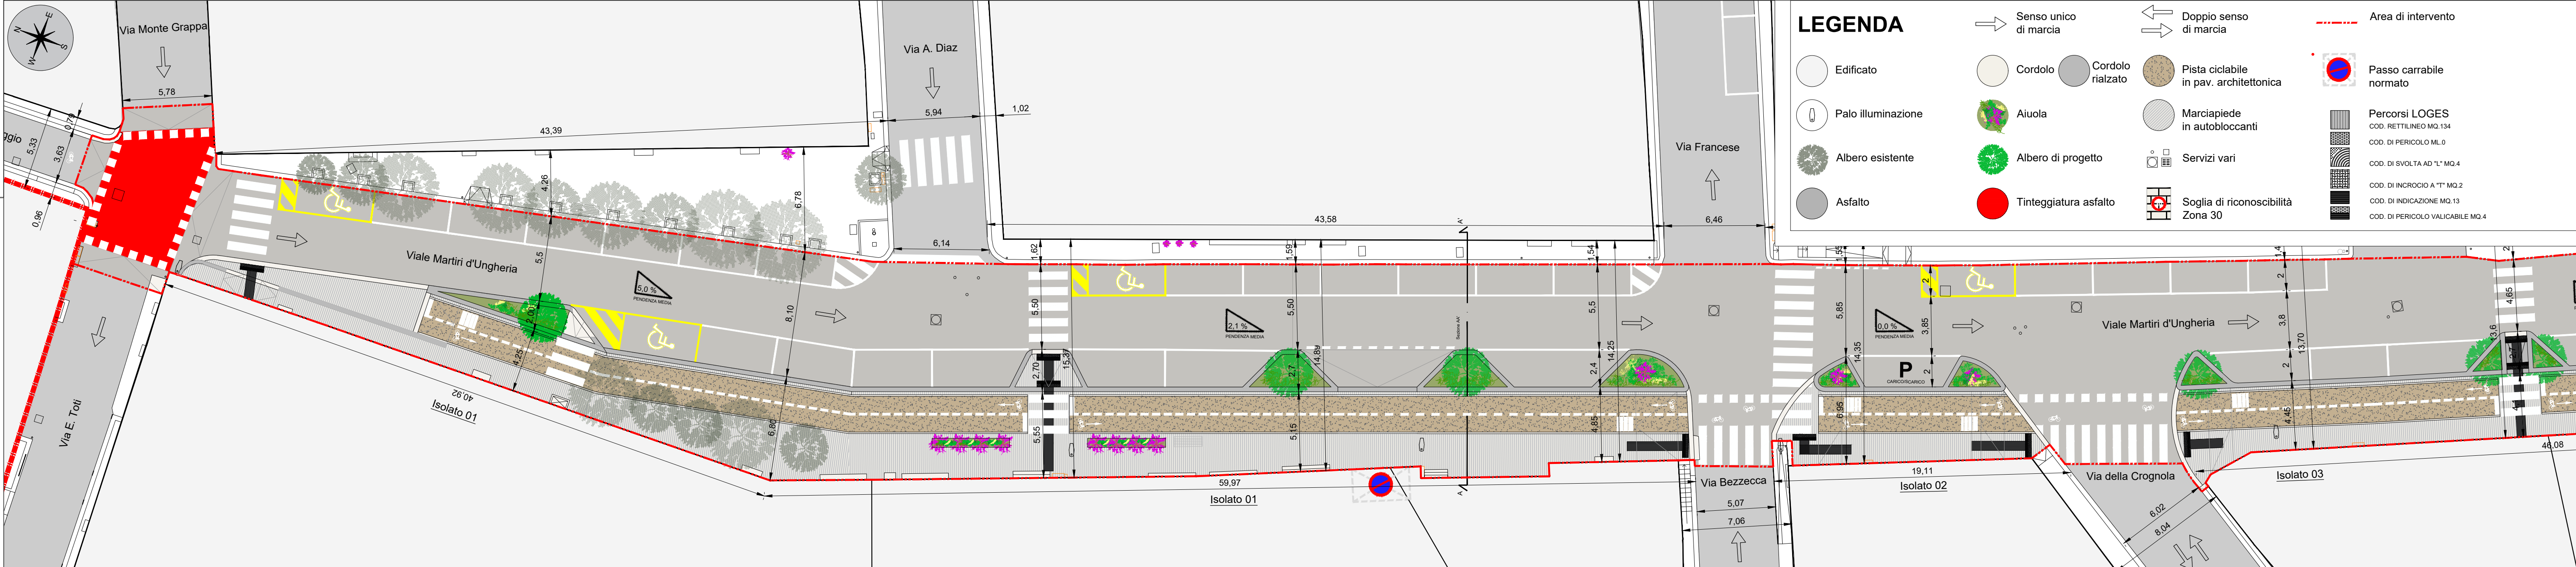


E_Viale Martiri d'Ungheria (Isolato 03 - 04 - 05 - 06 nel tratto compreso tra via Bainsizza a via Oslavia)

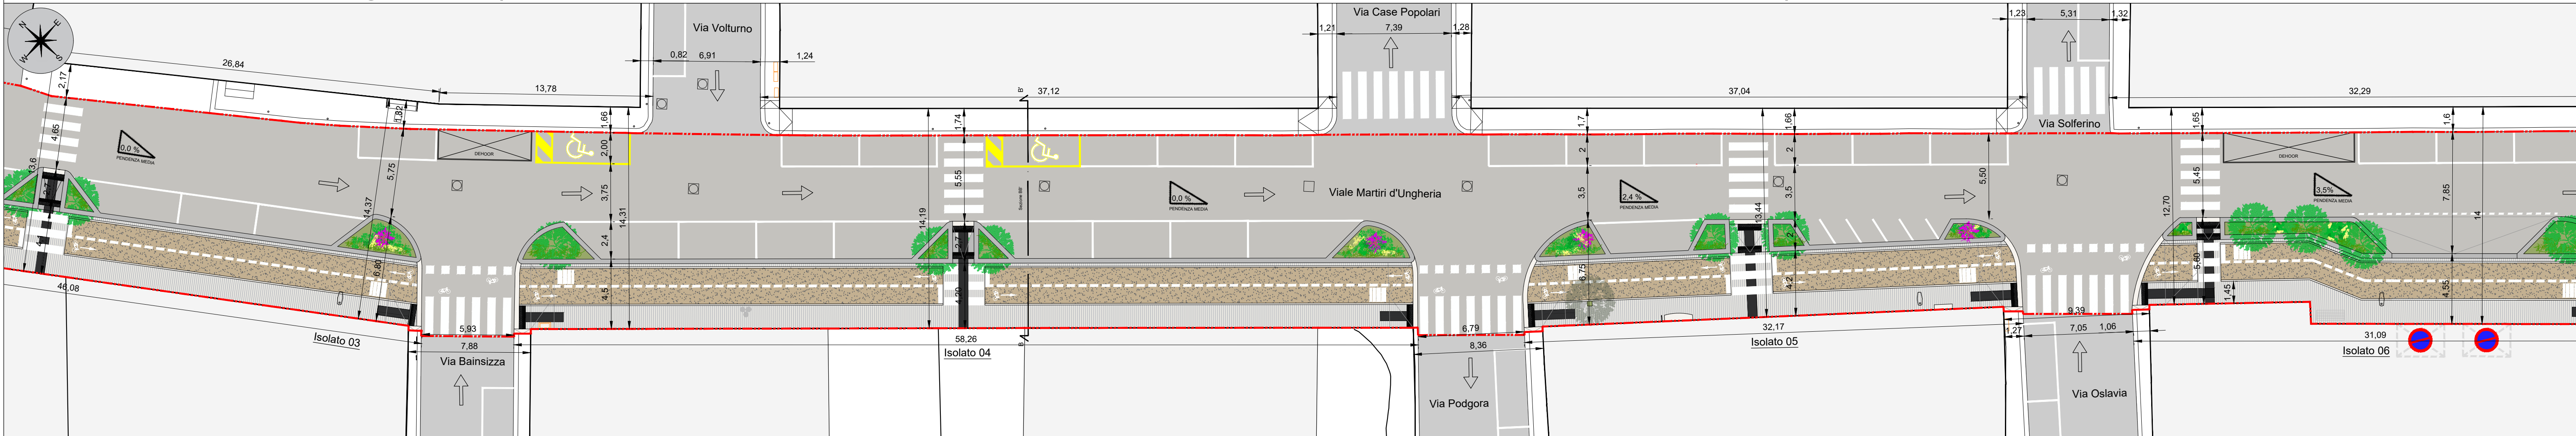

Dettaglio 01 - Viale Martiri d'Ungheria

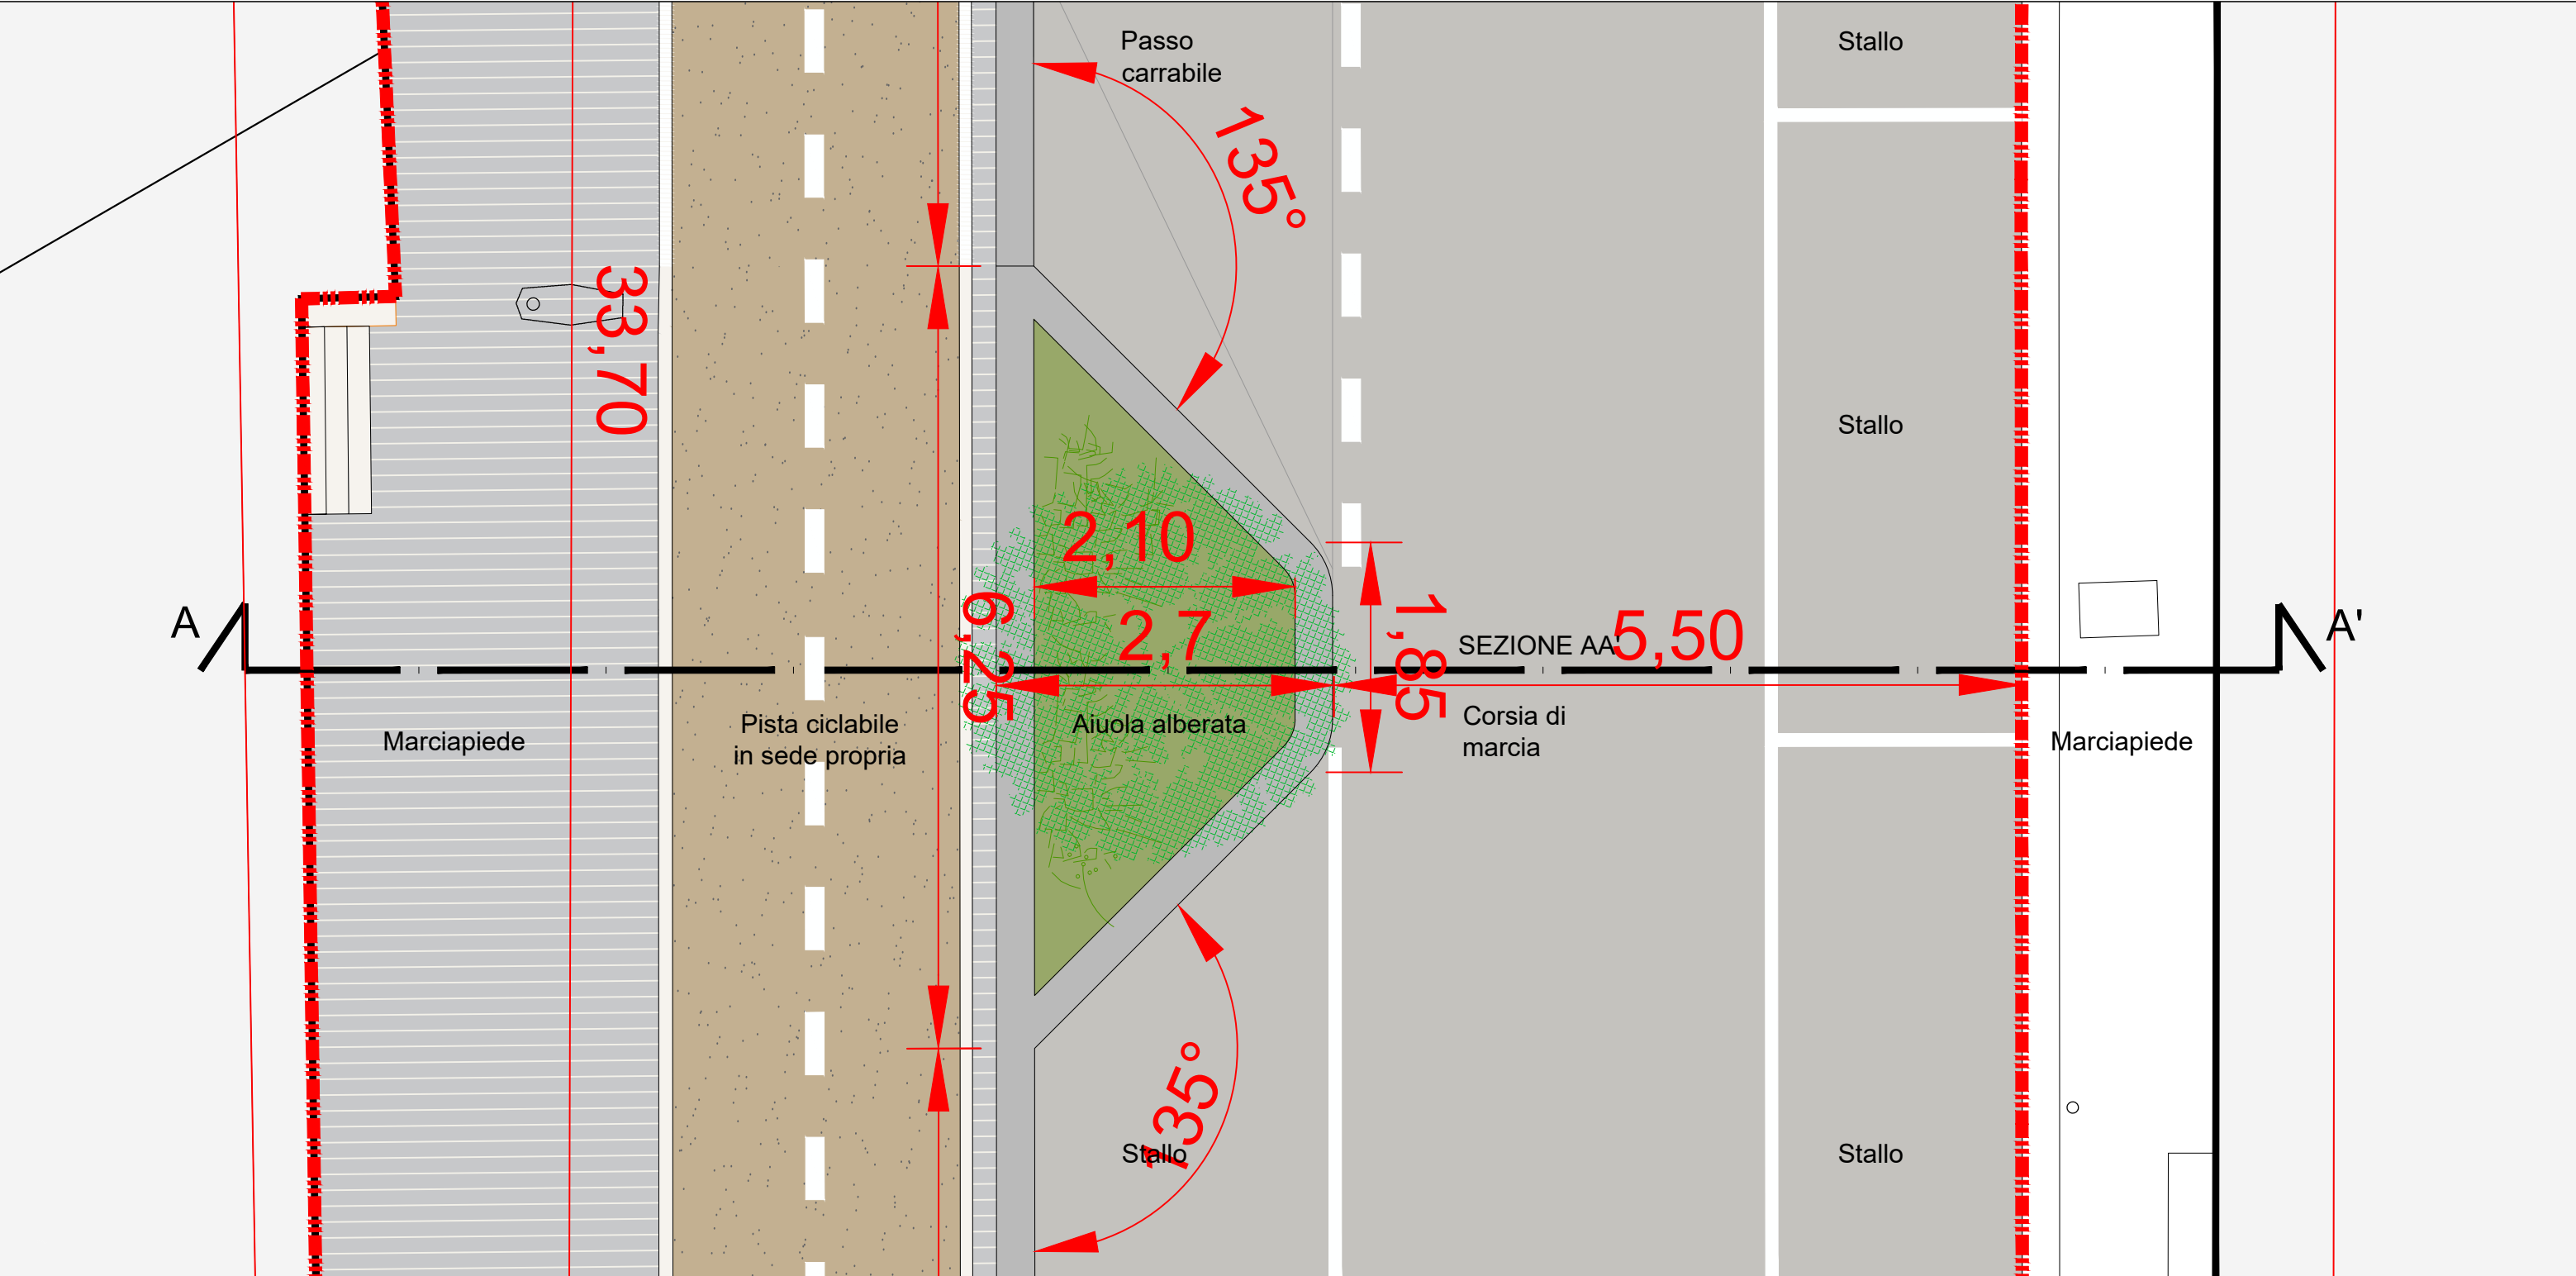

Sezione AA' - Viale Martiri d'Ungheria

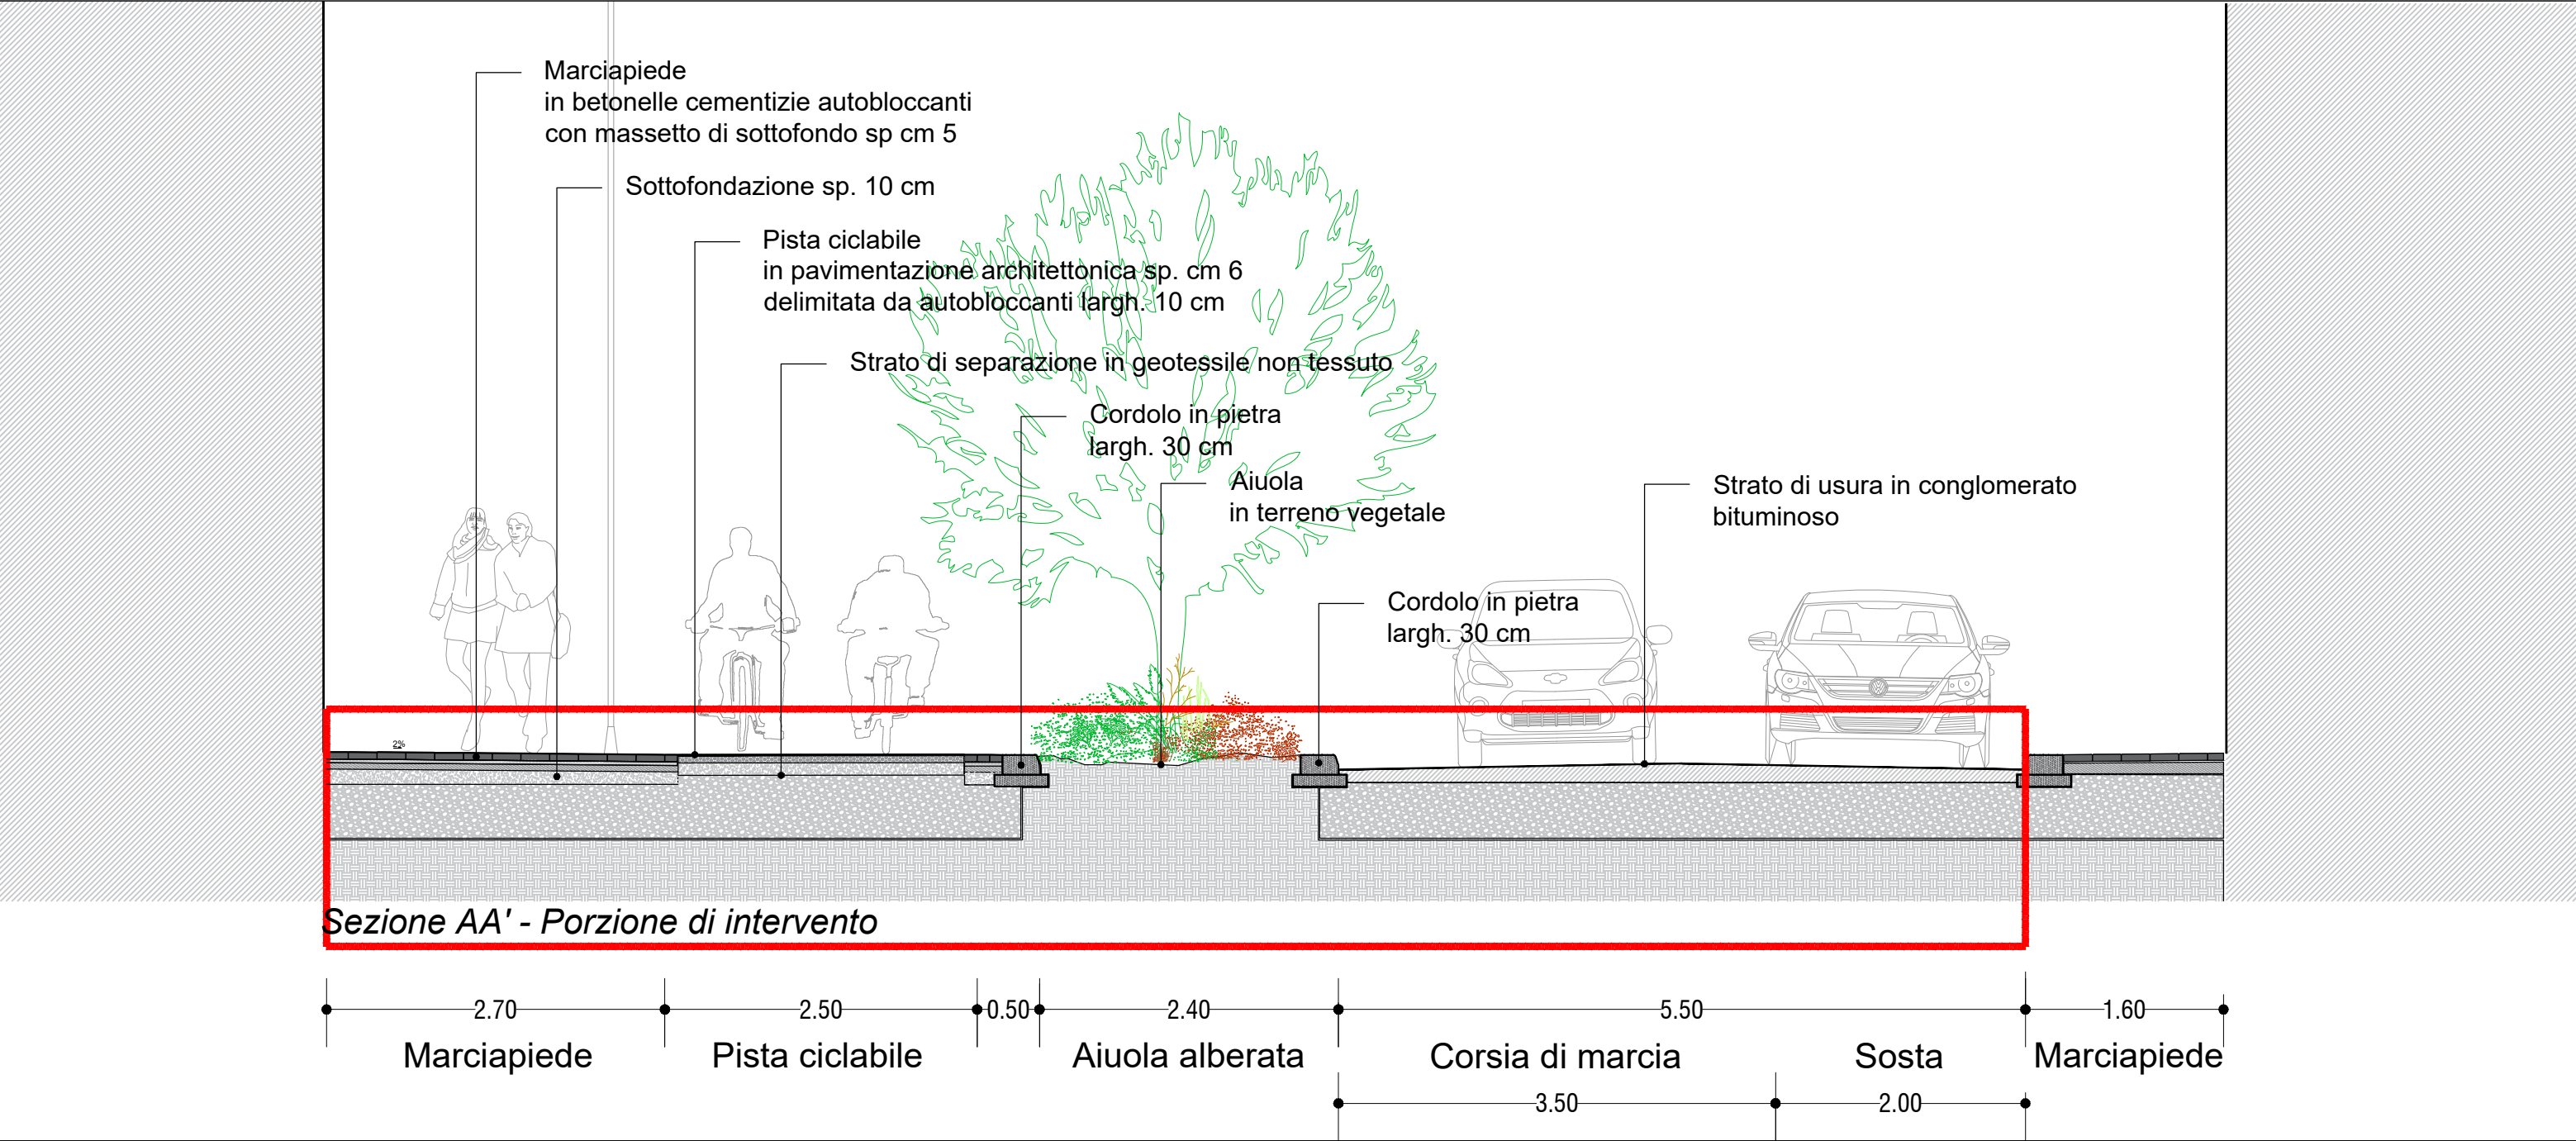

Sezione BB' - Viale Martiri d'Ungheria

